


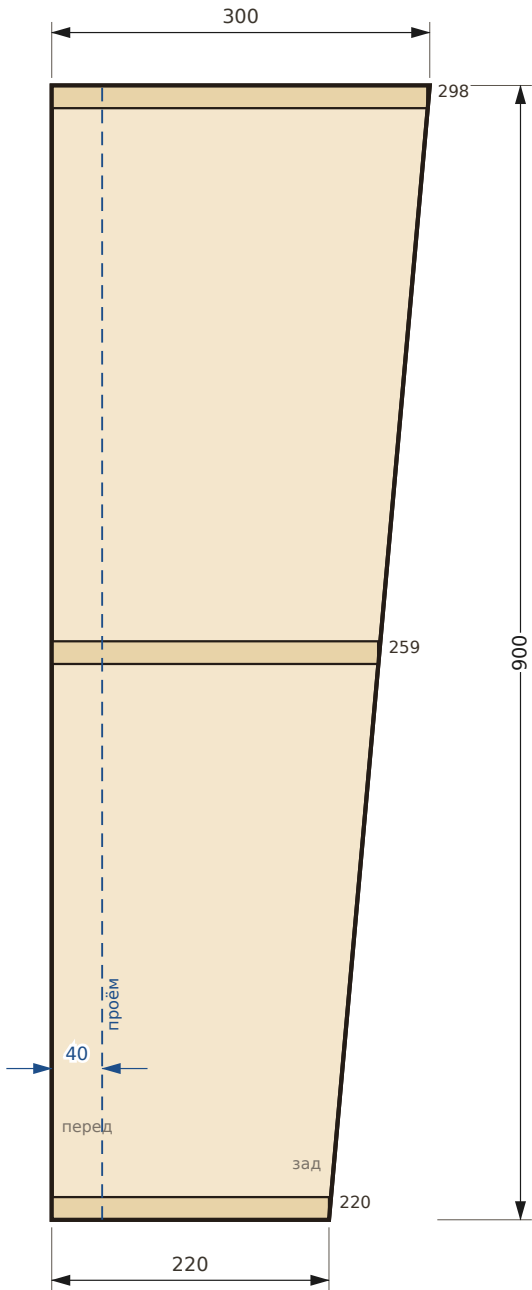

липа


**ГАБАРИТ**  
1290 × 900 мм  
глубина верх 300  
глубина низ 220

**ВЫСТУП 40 мм**  
уже входит в 300  
и в 220. Отдельно  
не прибавлять.  
Синяя линия —  
проём двери.

**СКОС**  
 $D = 220 + 80 \cdot H / 900$   
H — от пола, мм.  
Прямая вместо  
полукруглой стены.  
Подгонка по месту.

Верх не выше 900:  
не закрывать  
выключатель.

**ПОЛКИ**  
3 шт: низ на полу,  
середина, верх.  
Просветы по 423.  
Глубина полки —  
по нижней пласти.  
Пролёт 1254 мм:  
щит 18 может  
провиснуть, тогда  
стойка посередине  
или щит 20 мм.

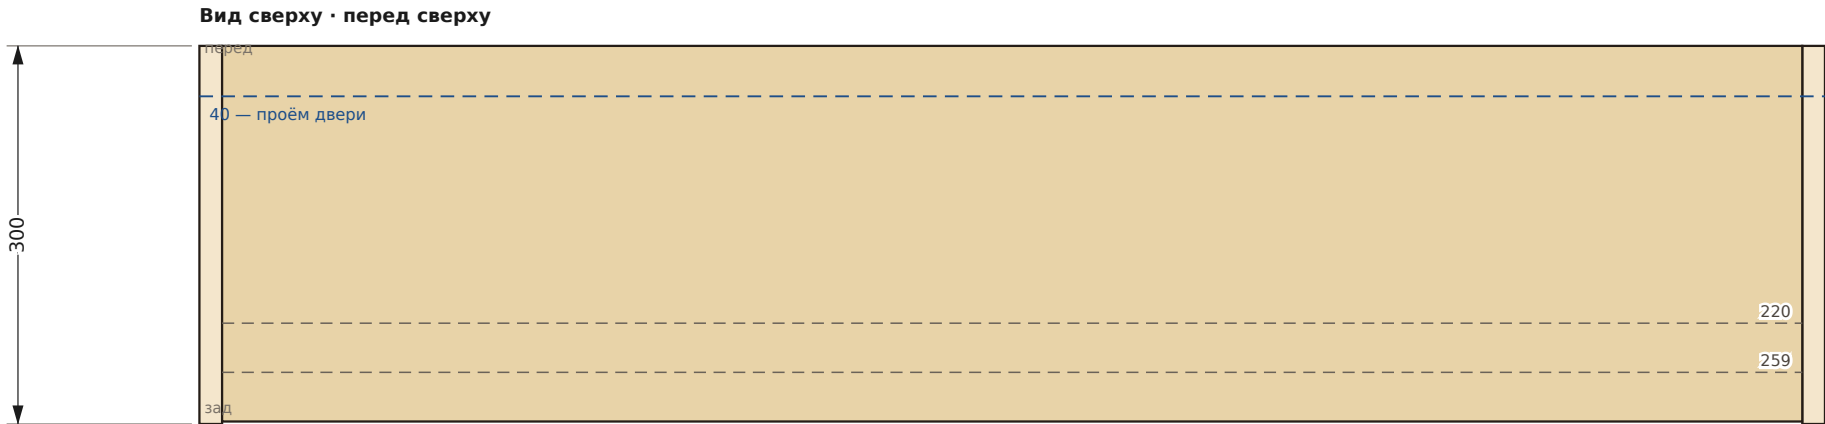

| Поз. | Наименование            | Кол. | Размер, мм           |
|------|-------------------------|------|----------------------|
| 1    | Боковина, трапеция      | 2    | 900 × 220...300 × 18 |
| 2    | Полка нижняя, верх 18   | 1    | 1254 × 220 × 18      |
| 3    | Полка средняя, верх 459 | 1    | 1254 × 259 × 18      |
| 4    | Полка верхняя, верх 900 | 1    | 1254 × 298 × 18      |



Контроль задней кромки боковины ≈ 904 мм.

ВАРИАНТ 1 · СТЕЛЛАЖ, 3 ПОЛКИ

Чертёж для производства · масштаб 1:6 · размеры в миллиметрах  
Первое приближение: заказчик уточняет размеры. Толщина щита 18 мм — принятая.  
Кромки шлифовать, без кромки ПВХ. Крепёж скрытый, шканты Ø8×30.

Материал  
**Щит липы**  
масло, тон стены  
образец до отделки

Лист  
**1 / 3**  
05.10.2026  
рев. 0

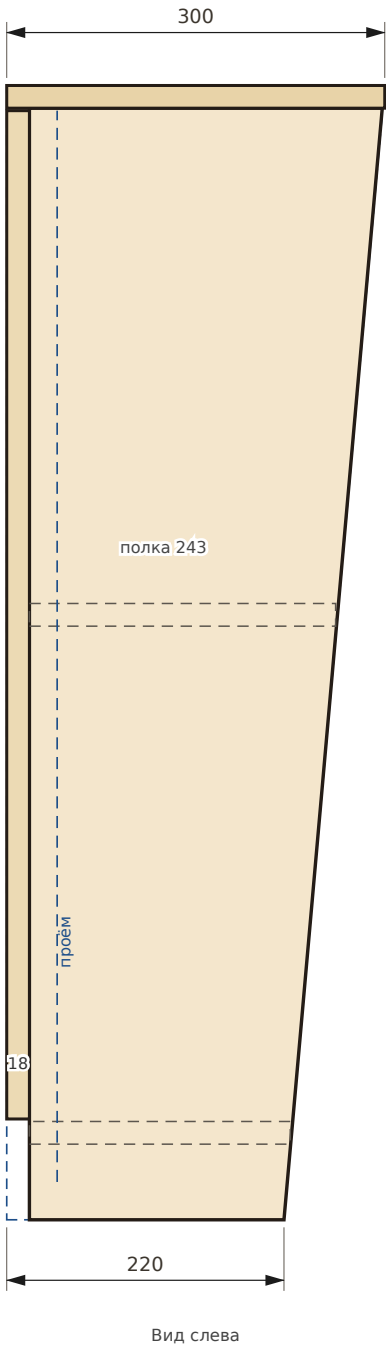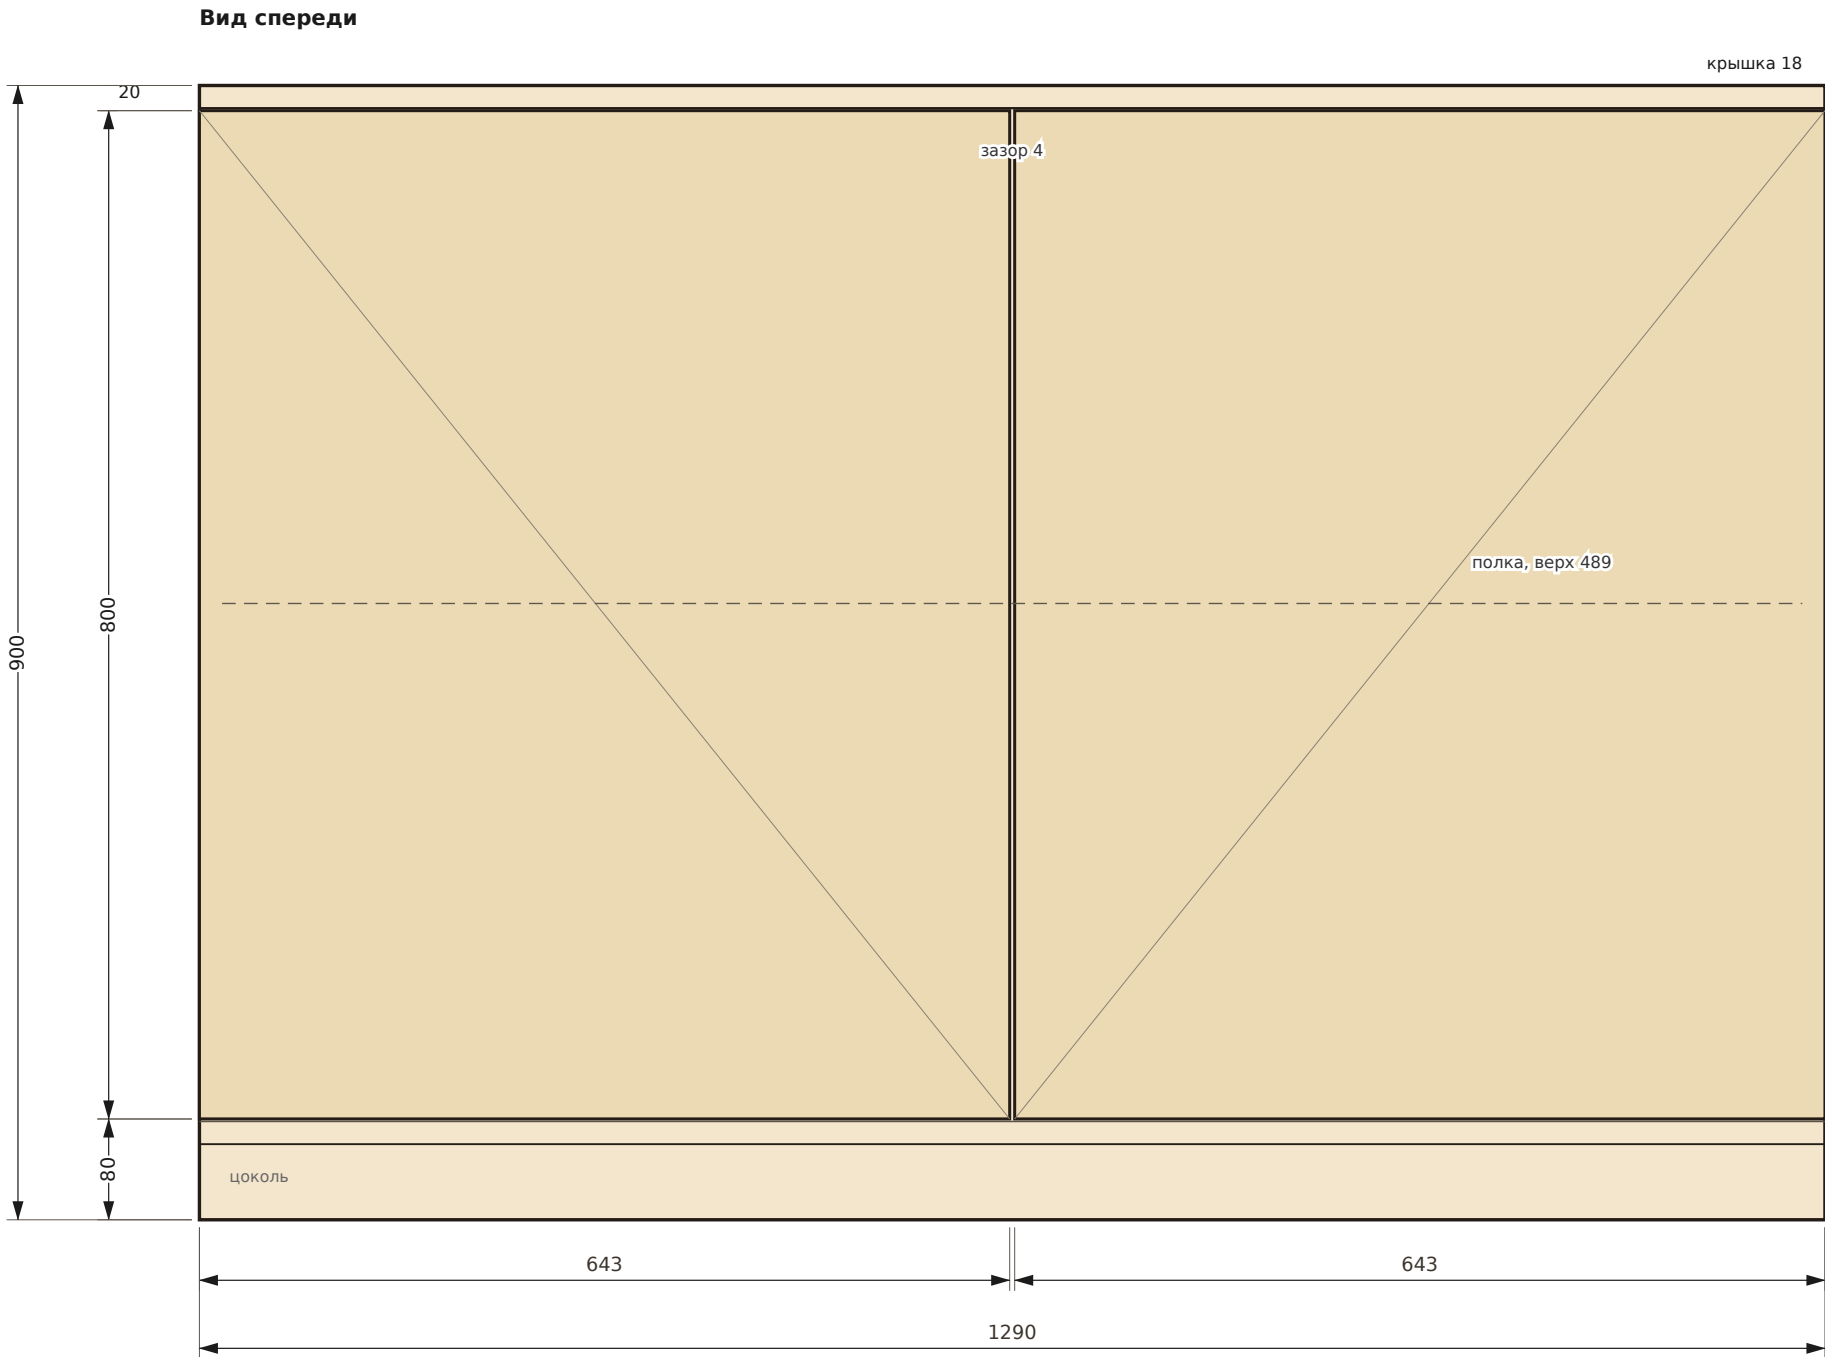

липа


**ГАБАРИТ**  
1290 × 900 мм  
глубина верх 300  
глубина низ 220

**ВЫСТУП 40 мм**  
уже входит в 300  
и в 220. Отдельно  
не прибавлять.  
Синяя линия —  
проём двери.

**СКОС**  
D = 220+80-H/900  
H — от пола, мм.  
Прямая вместо  
полукруглой стены.  
Подгонка по месту.

Верх не выше 900:  
не закрывать  
выключатель.

**ДВЕРКИ**  
Накладные, закрывают  
торцы боковин.  
Зазор между ними 4.  
Зазоры сверху  
и снизу по 2 мм.  
20 сверху =  
зазор 2 + крышка 18.  
Петли по 2 шт,  
100 мм от торцов.  
Ручки не сверлить.  
Цоколь утоплен  
на 18 мм.  
Полка по центру,  
просветы по 393.

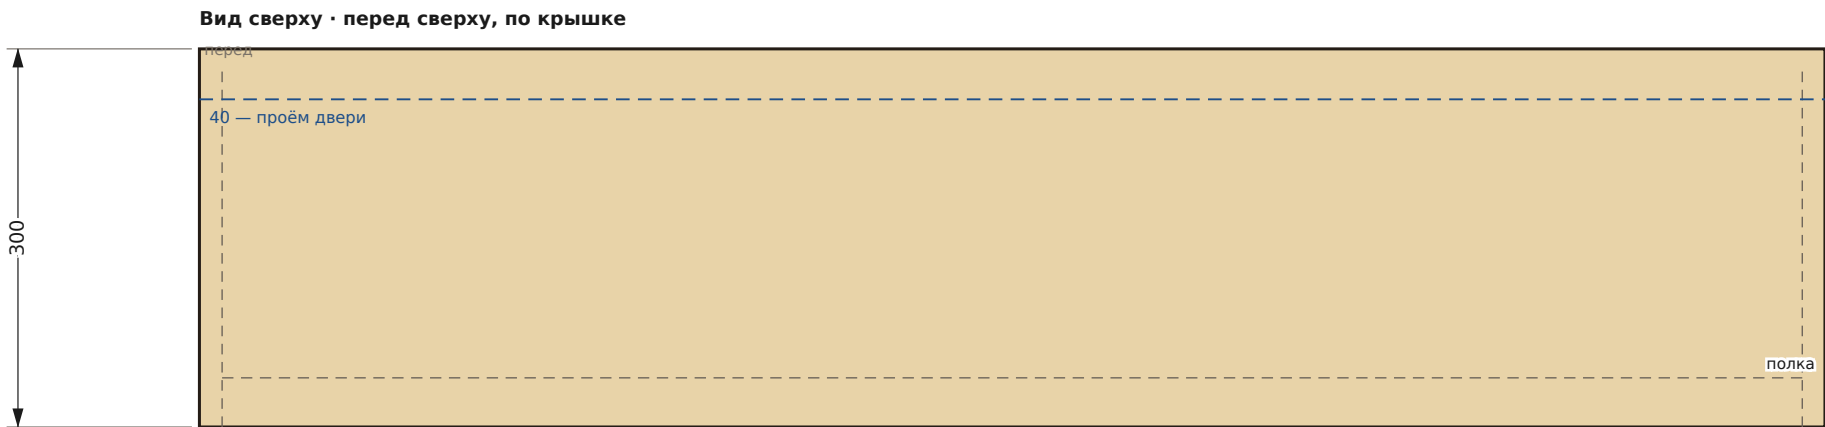

| Поз. | Наименование       | Кол. | Размер, мм           |
|------|--------------------|------|----------------------|
| 1    | Боковина, трапеция | 2    | 882 × 202...280 × 18 |
| 2    | Крышка накладная   | 1    | 1290 × 300 × 18      |
| 3    | Дно, верх 78       | 1    | 1254 × 207 × 18      |
| 4    | Полка, верх 489    | 1    | 1254 × 243 × 18      |
| 5    | Дверка накладная   | 2    | 643 × 800 × 18       |
| 6    | Цоколь             | 1    | 1254 × 60 × 18       |
| 7    | Петля Ø35, 110°    | 4    | вкладка 100 мм       |



Корпус утоплен на 18 мм: глубины деталей уже с этим вычетом.

ВАРИАНТ 2 · ТУМБА С ДВЕРКАМИ

Чертёж для производства · масштаб 1:6 · размеры в миллиметрах  
Первое приближение: заказчик уточняет размеры. Толщина щита 18 мм — принятая.  
Кромки шлифовать, без кромки ПВХ. Крепёж скрытый, шканты Ø8×30.

Материал  
**Щит липы**  
масло, тон стены  
образец до отделки

Лист  
**2 / 3**  
05.10.2026  
рев. 0

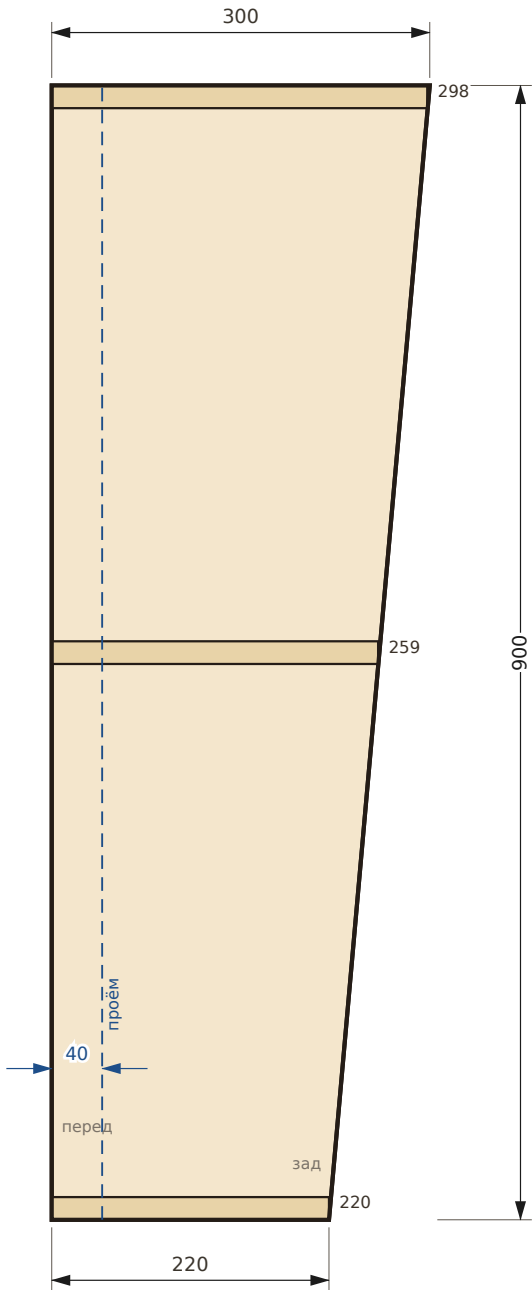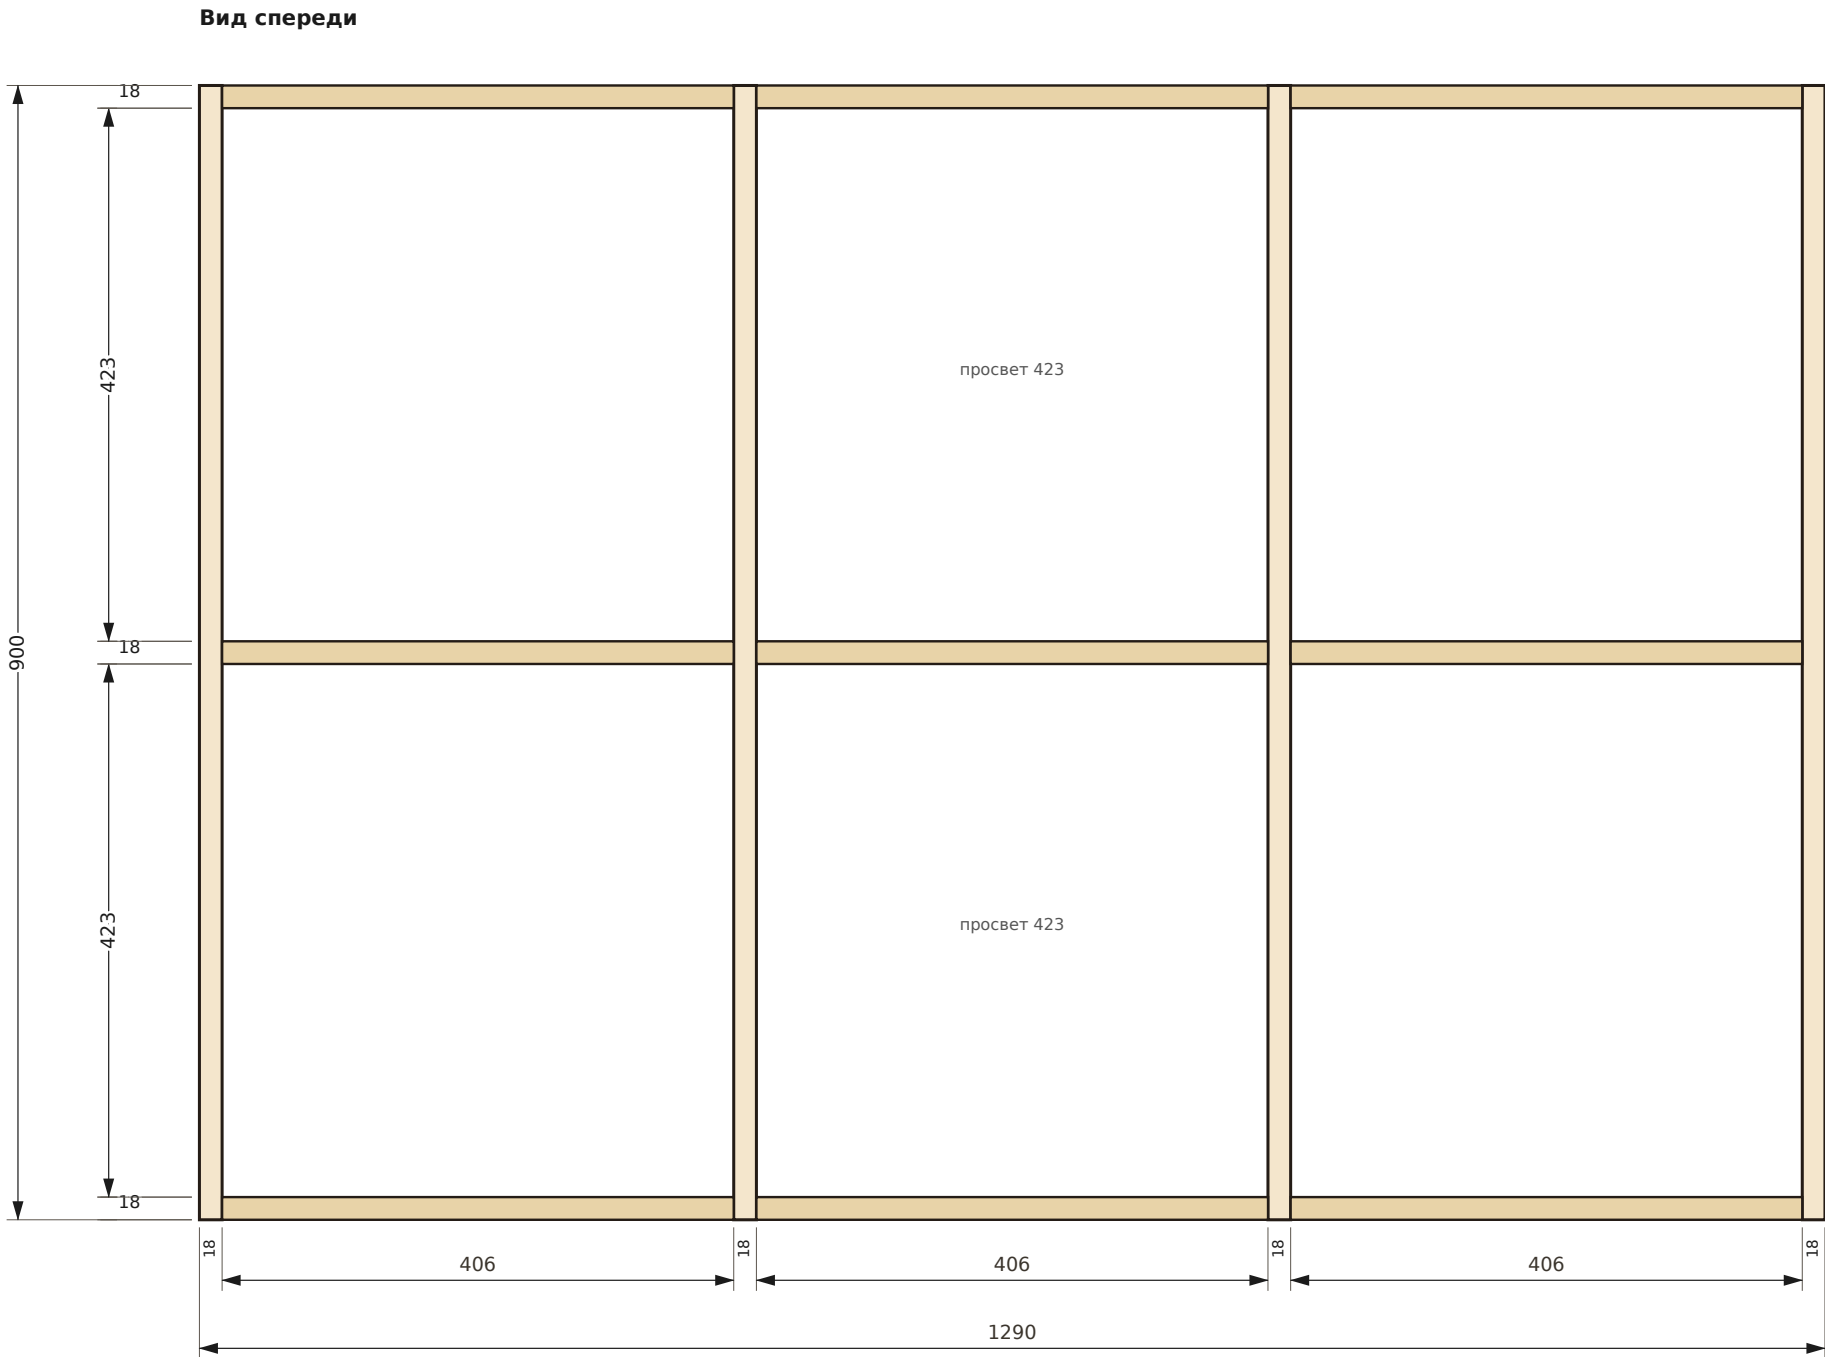

липа

**ГАБАРИТ**  
1290 × 900 мм  
глубина верх 300  
глубина низ 220

**ВЫСТУП 40 мм**  
уже входит в 300  
и в 220. Отдельно  
не прибавлять.  
Синяя линия —  
проём двери.

**СКОС**  
 $D = 220 + 80 \cdot H / 900$   
H — от пола, мм.  
Прямая вместо  
полукруглой стены.  
Подгонка по месту.


Верх не выше 900:  
не закрывать  
выключатель.

**6 ЯЧЕЕК**  
Два ряда, три  
отделения. Без  
дверок.  
Разделители — 2 шт  
на всю высоту,  
тот же скос,  
что у боковин.  
Полки вкладные:  
406 мм, по 3 шт  
на каждый ярус.  
Просветы по 423.

Вид слева: боковина и разделители

| Поз. | Наименование            | Кол. | Размер, мм           |
|------|-------------------------|------|----------------------|
| 1    | Боковина, трапеция      | 2    | 900 × 220...300 × 18 |
| 2    | Разделитель, трапеция   | 2    | 900 × 220...300 × 18 |
| 3    | Полка нижняя, верх 18   | 3    | 406 × 220 × 18       |
| 4    | Полка средняя, верх 459 | 3    | 406 × 259 × 18       |
| 5    | Полка верхняя, верх 900 | 3    | 406 × 298 × 18       |

Разделители пилить по тому же скосу, что и боковины.

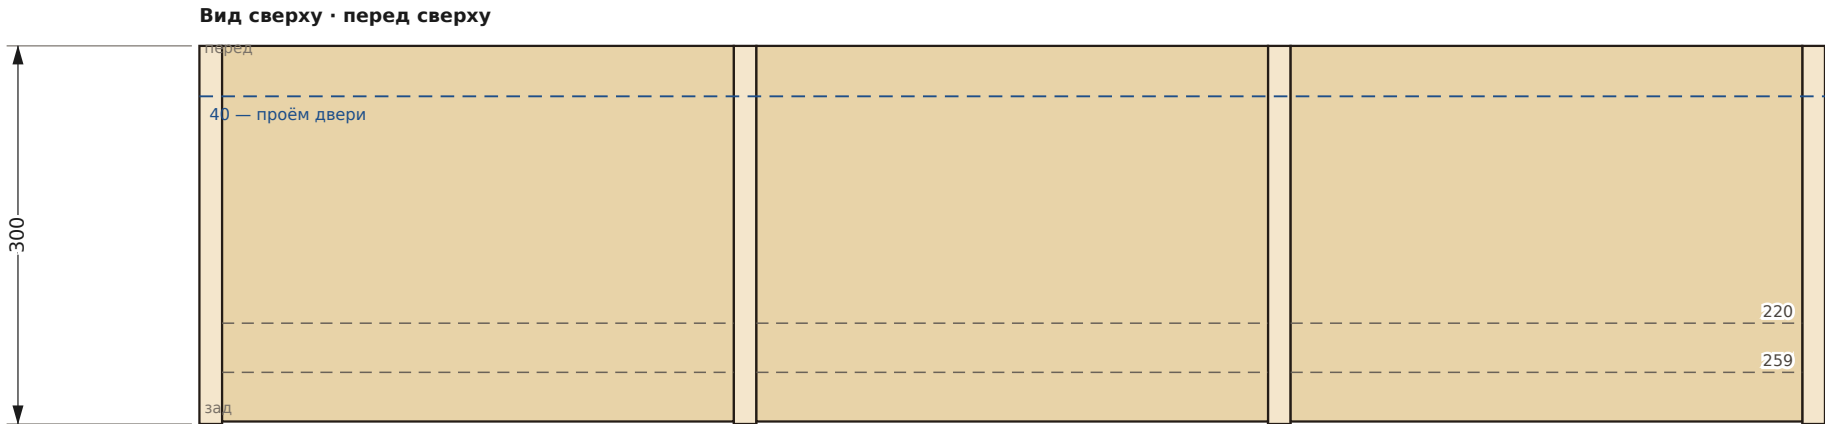

ВАРИАНТ 3 · ПОЛКИ, 6 ЯЧЕЕК

Чертёж для производства · масштаб 1:6 · размеры в миллиметрах  
Первое приближение: заказчик уточняет размеры. Толщина щита 18 мм — принятая.  
Кромки шлифовать, без кромки ПВХ. Крепёж скрытый, шканты Ø8×30.

Материал  
**Щит липы**  
масло, тон стены  
образец до отделки

Лист  
**3 / 3**  
05.10.2026  
рев. 0